

ISSUED FOR APPROVAL

CCA-SS1-EMDB-1A

ELECTRICAL DATA:		
Rated Operating voltage	V AC	400
Rated frequency	Hz	60
Rated current	A	1600
System Configuration		TNS, 3 PHASE, 4 WIRES
Rated control voltage	V AC	230
Rated control voltage	V DC	110
Rated insulation voltage	V	1000
Rated Impulse Withstand Voltage	KV	12

BUSBAR DETAILS:		
Main busbar cross section	mm	1x4x20x10
Neutral Busbar	mm	1x4x20x10
Ground Busbar	mm	1x2x20x5
Short Time Current (kA) for 1sec	Icw	35
Busbar treatment		Tin-plated Copper
Busbar Insulation		Yes
Color code		Red, Yellow, Blue, Black, Green/Yellow
Version of external connection		L1,L2,L3,N,PE

ENCLOSURE DETAILS:		
Type of Switchgear		Sivacon S8
Installation		Free Stand
Internal separation		Form 4b
Degree of protection	IP	43
Canopy		Yes
Ventilation		Yes
Gland plate		Yes
Color of enclosure		RAL 7035
Color of canopy		RAL 7035

CONNECTION DETAILS:		
Cable connection for supply cubicle(s)		Top/Bottom
Cable connection for outgoing cubicle(s)		Top/Bottom
Connection in plant		Front

SERVICE LOCATION:		
Installation Area		Indoor
Ambient temperature	°C	50
Altitude	m	<2000

WIRING:		
Wires type		PVC 450-750 V, Cu, LS0H
Control circuit cross section	mm²	1.5
CT circuit cross section	mm²	2.5
Auxiliary power circuit cross section	mm²	1.5
AC circuit color		Red, Black
DC circuit color		Grey
CT circuit color		Red, Yellow, Blue
Auxiliary power circuit color		Red, Black
Labeling		Cable Numbers

IDENTIFICATION LABEL:		
Material		Gravoply
Color		White Text in Black Background
Language		English
Fixation		Adhesive Glue

REVISION					
REV	DESCRIPTION	PREP	CHKD	APPD	DATE
R02	FOR APPROVAL	STM	SAK	SAK	13/07/26
R01	FOR APPROVAL	STM	SAK	SAK	16/06/26
R00	FOR APPROVAL	STM	SAK	SAK	20/03/25

PROJECT
KING KHALID INTERNATIONAL
AIRPORT (KKIA) PROJECT
CONCOURSE-A

CLIENT

ENGINEER



CONTRACTOR

DRAWING TITLE
CCA-SS1-EMDB-1A



DATA SHEET			
MANUFACTURER	DRAWING NO. CCA-SS1-EMDB-1A		
	PROJECT REFERENCE:		REC. 00
	SCALE : NTS	LOCATION: +	SIZE: A4
	SHEET NO:	1 of 24	

QUOTATION REF.


FILE NAME: 07_CCA-SS1-EMDB-1A

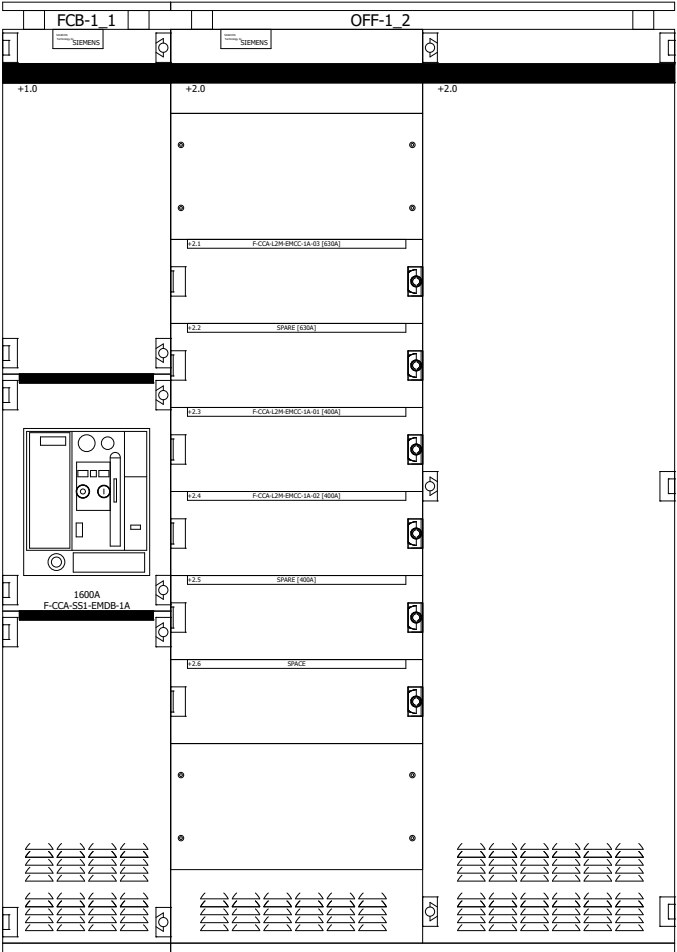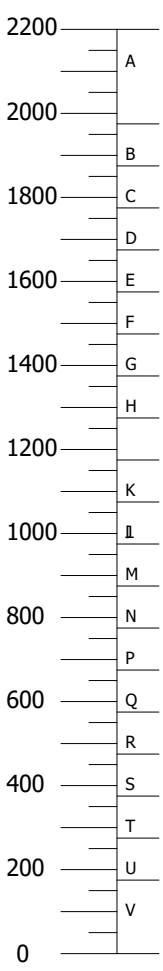


FRONT VIEW

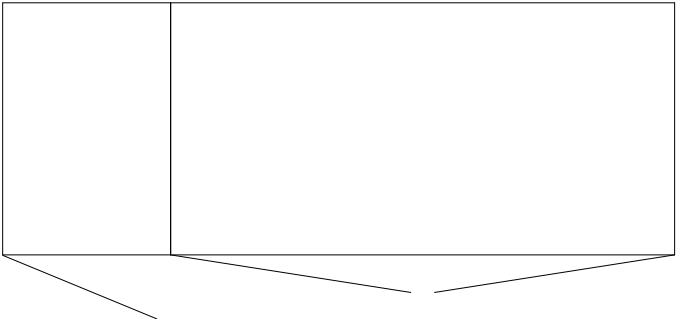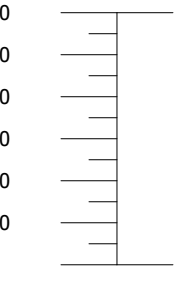

TOP VIEW

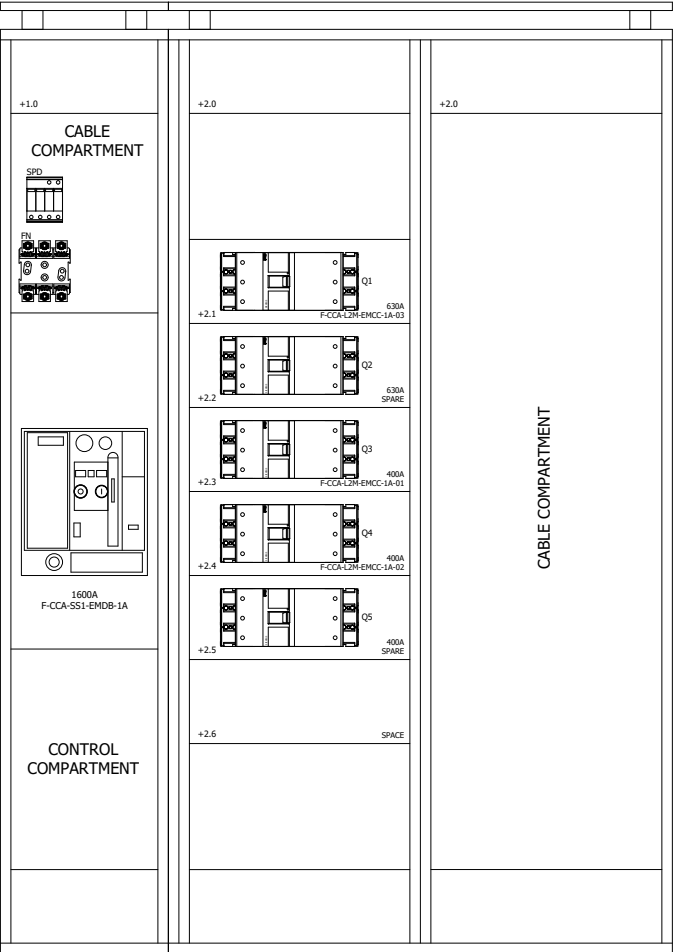

INTERNAL VIEW

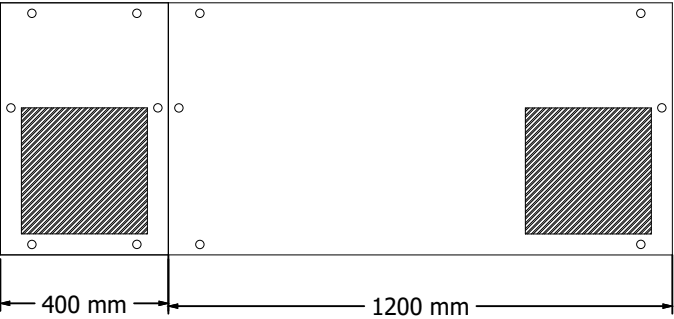

BOTTOM VIEW

REVISION					
REV	DESCRIPTION	PREP	CHKD	APPD	DATE

R02	FOR APPROVAL	STM	SAK	SAK	13/07/26
R01	FOR APPROVAL	STM	SAK	SAK	16/06/26
R00	FOR APPROVAL	STM	SAK	SAK	20/03/25

PROJECT
KING KHALID INTERNATIONAL
AIRPORT (KKIA) PROJECT
CONCOURSE-A

CLIENT

ENGINEER

CONTRACTOR


DRAWING TITLE
CCA-SS1-EMDB-1A

GENERAL ARRANGEMENT

MANUFACTURER	DRAWING NO. CCA-SS1-EMDB-1A		
	PROJECT REFERENCE:		REC. 00
	SCALE : NTS	LOCATION: +	SIZE: A4
	SHEET NO: 2 of 24		

QUOTATION REF.

FILE NAME: 07_CCA-SS1-EMDB-1A

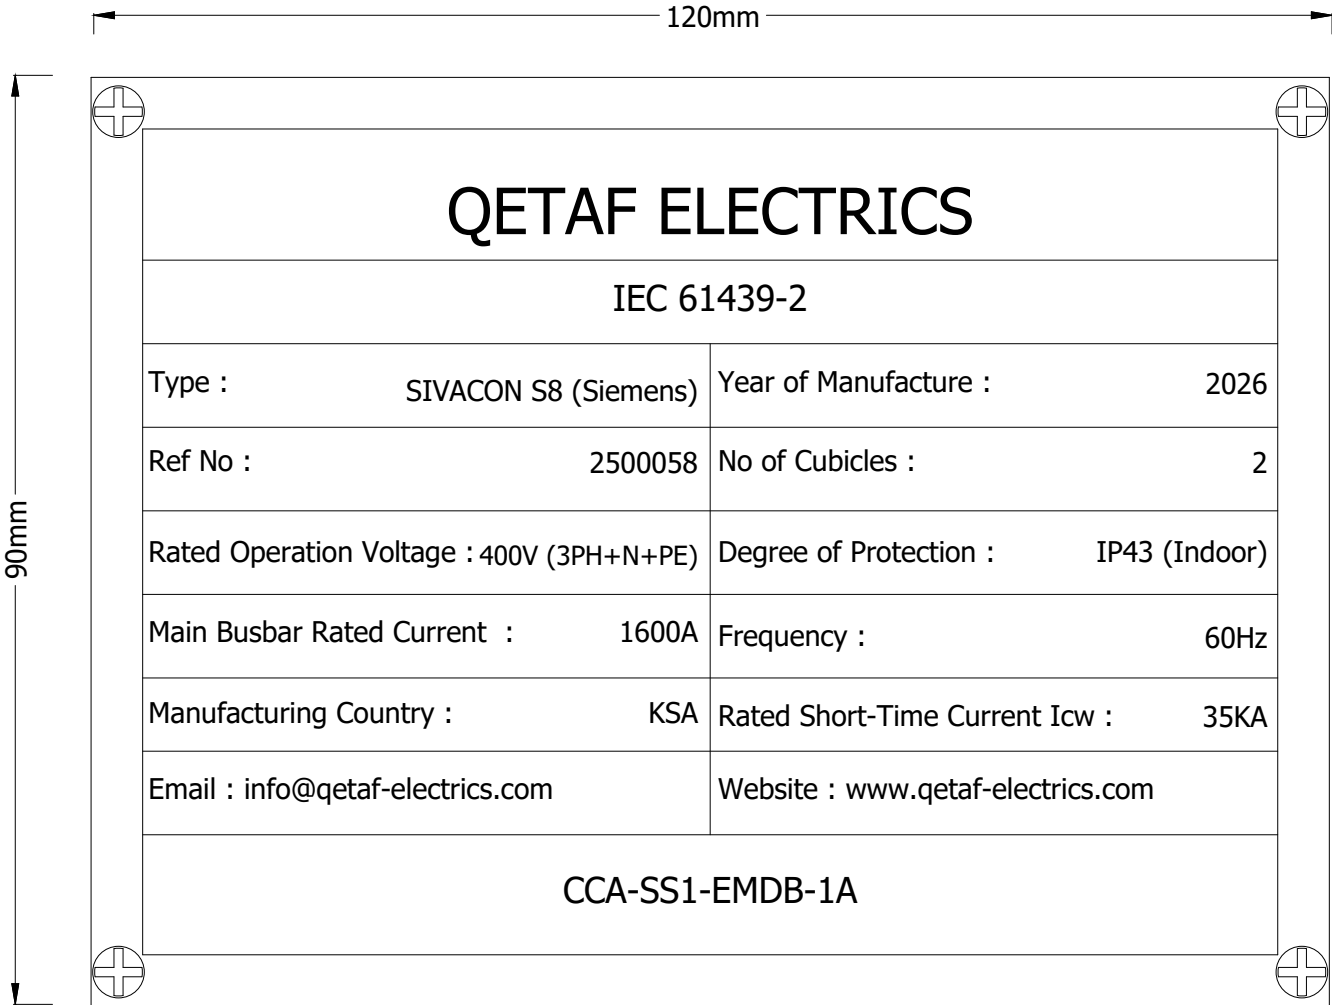

REVISION					
REV	DESCRIPTION	PREP	CHKD	APPD	DATE
R02	FOR APPROVAL	STM	SAK	SAK	13/07/26
R01	FOR APPROVAL	STM	SAK	SAK	16/06/26
R00	FOR APPROVAL	STM	SAK	SAK	20/03/25

PROJECT
KING KHALID INTERNATIONAL
AIRPORT (KKIA) PROJECT
CONCOURSE-A

CLIENT

ENGINEER

CONTRACTOR


DRAWING TITLE
CCA-SS1-EMDB-1A

NAME PLATE

MANUFACTURER	DRAWING NO. CCA-SS1-EMDB-1A		
	PROJECT REFERENCE:		REC. 00
	SCALE : NTS	LOCATION: +	SIZE: A4
	SHEET NO:	3 of 24	

QUOTATION REF.

FILE NAME: 07_CCA-SS1-EMDB-1A

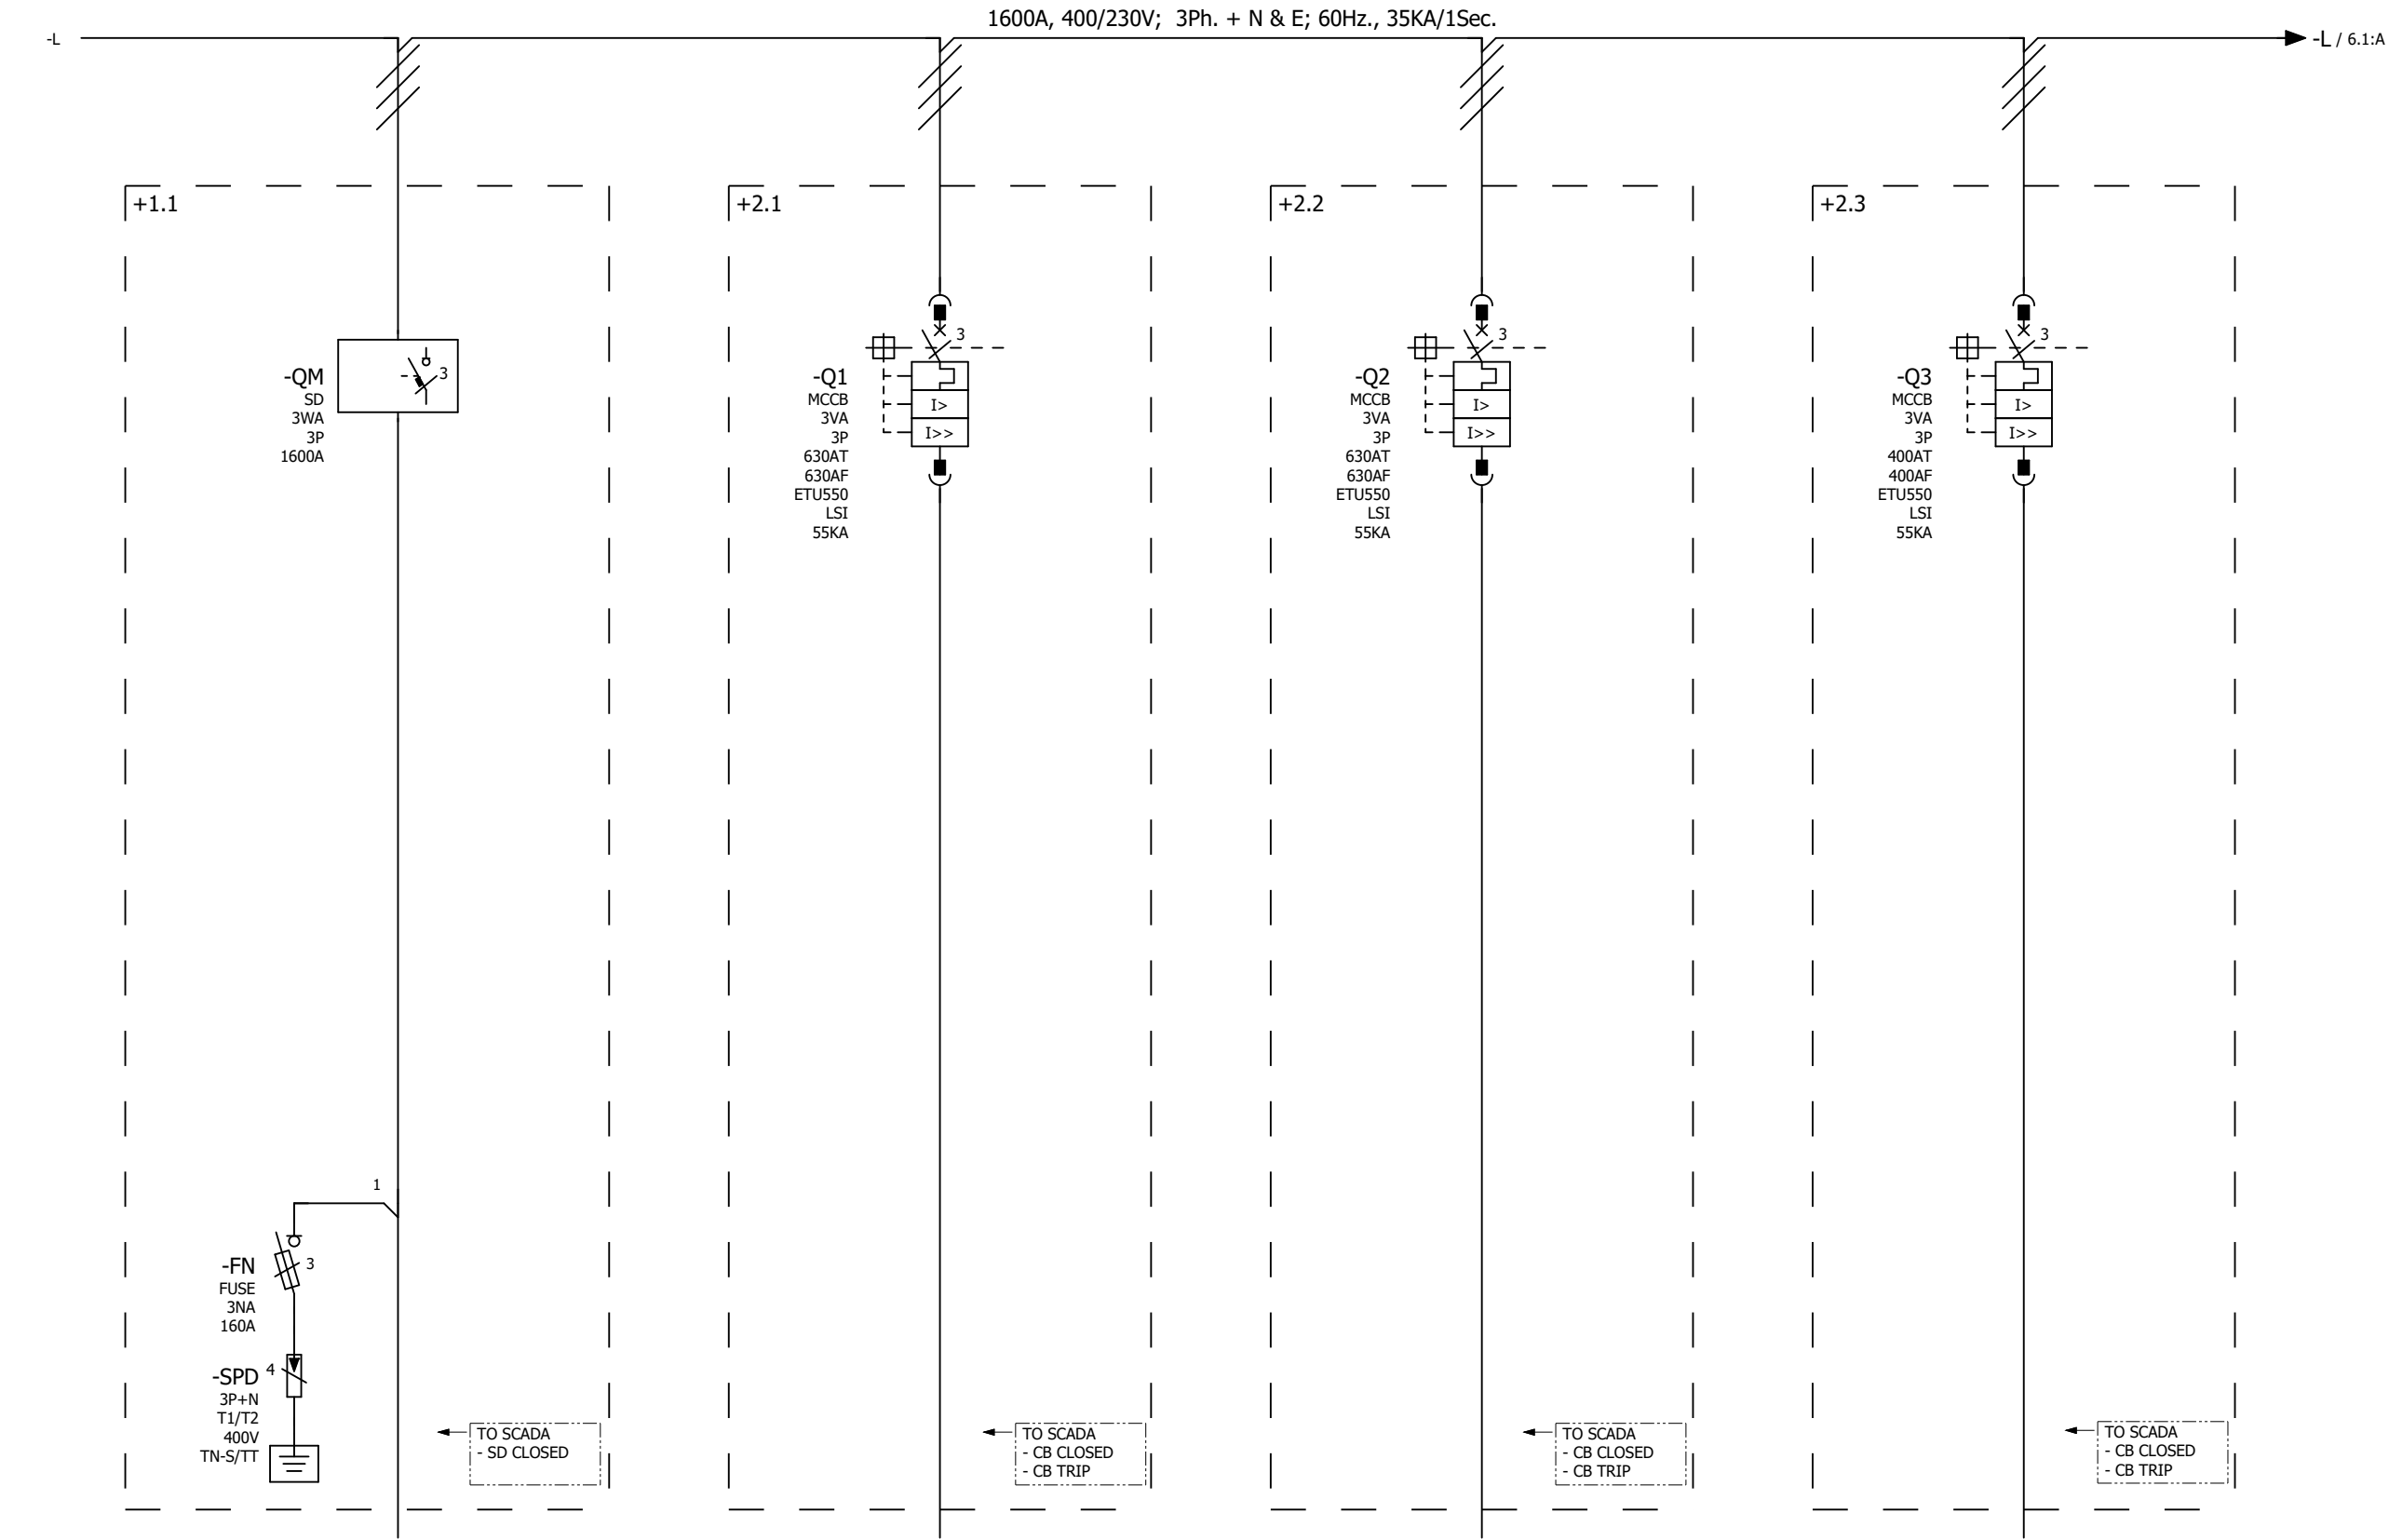

AMP. RATING	1600A	630A	630A	400A
LOAD	-	225KVA	-	206.25KVA
SERVICE	F-CCA-SS1-EMDB-1A	F-CCA-L2M-EMCC-1A-03	SPARE	F-CCA-L2M-EMCC-1A-01
CABLE SIZE	3x(4C x 300) mm ² + 1x(1C x 150) mm ² (E)	4x(4C x 240) mm ² CU/MICA/XLPE/SWA/LSZH + 4x(1C x 120) mm ² CU/LSZH (E)	-	2x(4C x 240) mm ² CU/MICA/XLPE/SWA/LSZH + 4x(1C x 120) mm ² CU/LSZH (E)

REVISION					
REV	DESCRIPTION	PREP	CHKD	APPD	DATE
R02	FOR APPROVAL	STM	SAK	SAK	13/07/26
R01	FOR APPROVAL	STM	SAK	SAK	16/06/26
R00	FOR APPROVAL	STM	SAK	SAK	20/03/25

PROJECT

KING KHALID INTERNATIONAL
AIRPORT (KKIA) PROJECT
CONCOURSE-A

CLIENT

ENGINEER

CONTRACTOR

DRAWING TITLE


CCA-SS1-EMDB-1A

SINGLE LINE DIAGRAM

MANUFACTURER	DRAWING NO. CCA-SS1-EMDB-1A		
	PROJECT REFERENCE:		REC. 00
	SCALE : NTS	LOCATION: +	SIZE: A4
	SHEET NO:	5 of 24	

QUOTATION REF.

FILE NAME: 07_CCA-SS1-EMDB-1A

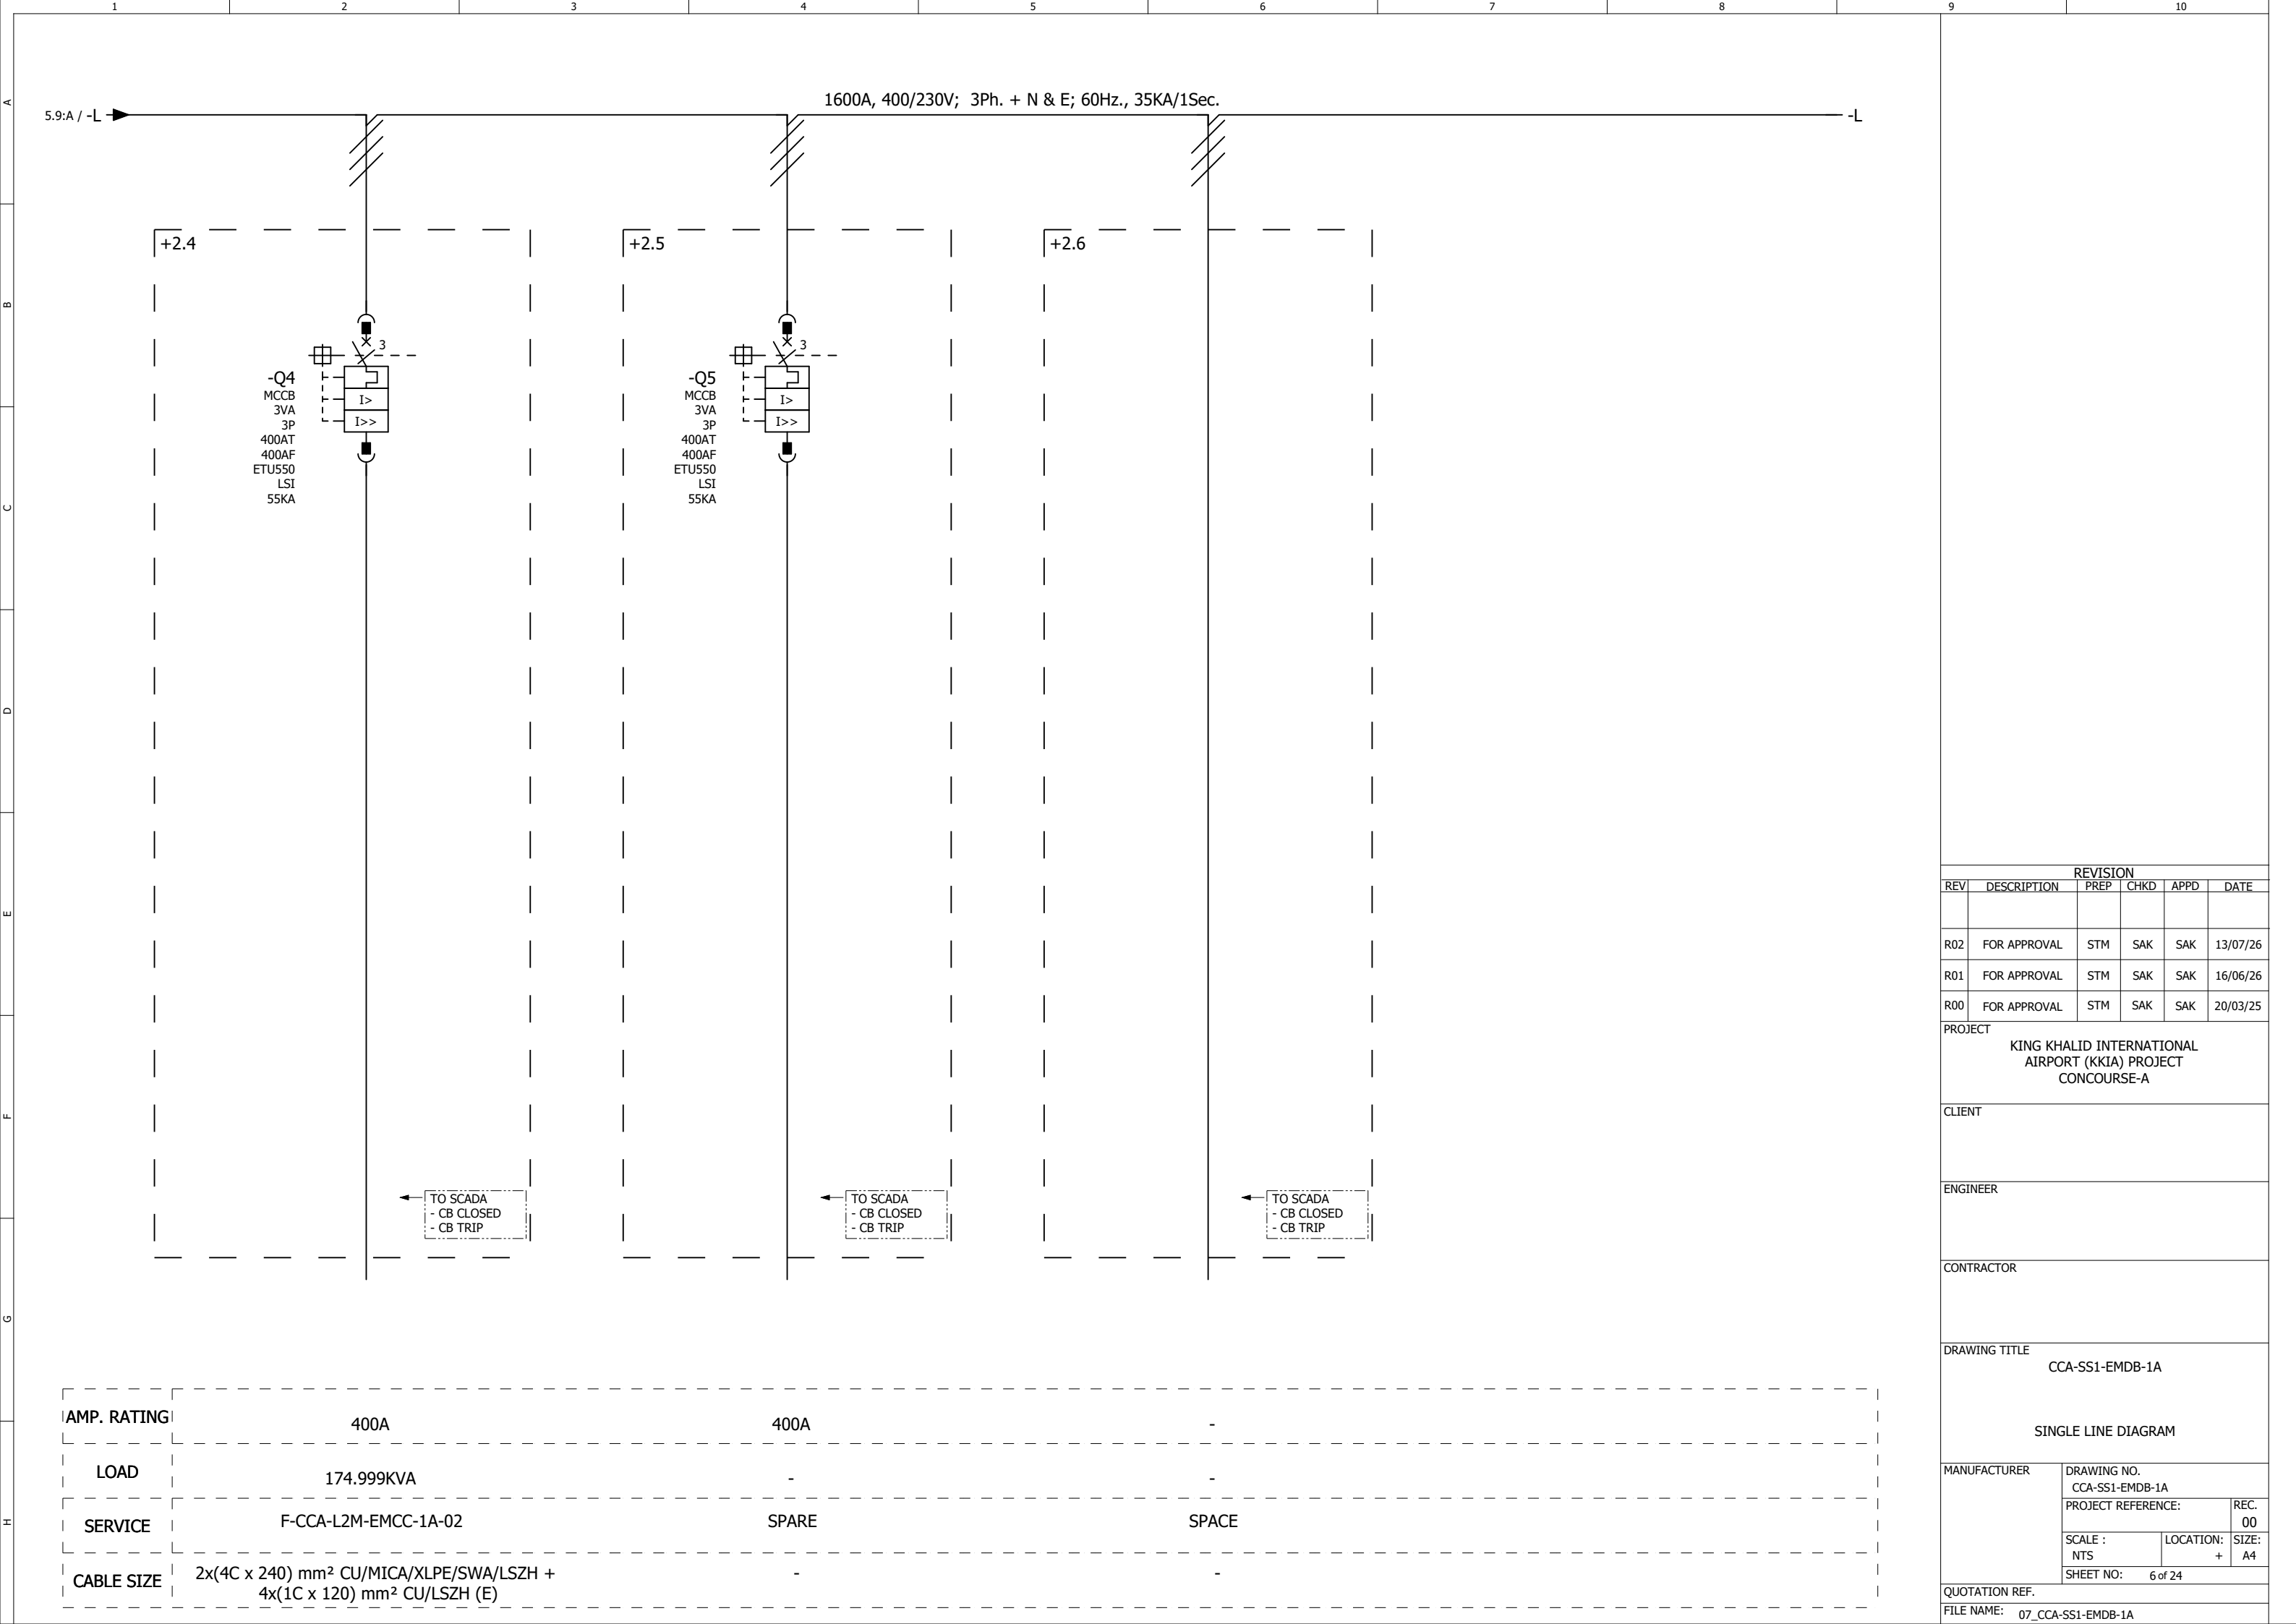

REVISION					
REV	DESCRIPTION	PREP	CHKD	APPD	DATE
R02	FOR APPROVAL	STM	SAK	SAK	13/07/26
R01	FOR APPROVAL	STM	SAK	SAK	16/06/26
R00	FOR APPROVAL	STM	SAK	SAK	20/03/25

PROJECT

KING KHALID INTERNATIONAL
AIRPORT (KKIA) PROJECT
CONCOURSE-A

CLIENT

ENGINEER

CONTRACTOR

DRAWING TITLE

CCA-SS1-EMDB-1A

SINGLE LINE DIAGRAM

MANUFACTURER	DRAWING NO. CCA-SS1-EMDB-1A		
	PROJECT REFERENCE:		REC. 00
	SCALE : NTS	LOCATION: +	SIZE: A4
	SHEET NO:	6 of 24	

QUOTATION REF.

FILE NAME: 07_CCA-SS1-EMDB-1A

Device tag list

-FN		+ / 6.2: F
3NA3836		3
3NH4030		1
-QM		+ / 6.2: C
3WA1116-2CA02-0AA0		1
-SPD		+ / 6.2: G
5SD7414-3		1

REVISION					
REV	DESCRIPTION	PREP	CHKD	APPD	DATE
R02	FOR APPROVAL	STM	SAK	SAK	13/07/26
R01	FOR APPROVAL	STM	SAK	SAK	16/06/26
R00	FOR APPROVAL	STM	SAK	SAK	20/03/25
PROJECT					
KING KHALID INTERNATIONAL AIRPORT (KKIA) PROJECT CONCOURSE-A					
CLIENT					
ENGINEER					
CONTRACTOR					
DRAWING TITLE					
CCA-SS1-EMDB-1A					
DEVICE TAG LIST					
MANUFACTURER		DRAWING NO. CCA-SS1-EMDB-1A			
		PROJECT REFERENCE:			REC. 00
		SCALE : NTS		LOCATION: +1.1	SIZE: A4
		SHEET NO: 7 of 24			
QUOTATION REF.					
FILE NAME: 07_CCA-SS1-EMDB-1A					

Bill of Material

Order number	Qty.	Description	Make
3NA3836	3	LV HRC fuse element, NH00, In: 160 A, gG, Un AC: 500 V, Un DC: 250 V, Front indicator, live grip lugs	SIEMENS
3NH4030	1	LV HRC FUSE BASE, 690V(1000V) TRIPLE-POLE, 160A, SIZE 00	SIEMENS
3WA1116-2CA02-0AA0	1	Non-automatic circuit breaker Fixed-mounted version, IEC 60947-2, frame size 1, 3-poles, In=1600A up to 690V AC 50/60Hz, breaking capacity N Icc=55/42kA at 500/690V, without electr. trip unit ETU, rear connection horizontal, able to communication, Manual operating mechanism with mechanical closing, without Spring charging motor, Ready-to-close signal. switch, Auxiliary switches 2NO+2NC, without Closing coil (CC), manual operating mechanism with mechanical closing, without Remote trip alarm reset coil (RR), without 2nd shunt trip, without 1st Shunt trip	SIEMENS
5SD7414-3	1	LIGHTNING CONDUCTOR T1/T2, UN 240/400 V, UC 335/264 V A.C., PLUGGABLE PROTECTIVE MODULES, 3+1 CIRCUIT (TN-S, TT), WIDTH 72 MM WITH REMOTE SIGNALING	SIEMENS

REVISION					
REV	DESCRIPTION	PREP	CHKD	APPD	DATE

R02	FOR APPROVAL	STM	SAK	SAK	13/07/26
R01	FOR APPROVAL	STM	SAK	SAK	16/06/26
R00	FOR APPROVAL	STM	SAK	SAK	20/03/25

PROJECT	KING KHALID INTERNATIONAL AIRPORT (KKIA) PROJECT CONCOURSE-A
---------	--

CLIENT

ENGINEER

CONTRACTOR	

DRAWING TITLE

CCA-SS1-EMDB-1A

XXXXXXXXXXXXXXXXXXXX

SUMMARIZED PARTS LIST			
MANUFACTURER	DRAWING NO. CCA-SS1-EMDB-1A		
	PROJECT REFERENCE:		REC. 00
	SCALE : NTS	LOCATION: +1.1	SIZE: A4
	SHEET NO: 8 of 24		

QUOTATION REF.

FILE NAME: 07_CCA-SS1-EMDB-1A

Device tag list

[illegible]

REVISION					
REV	DESCRIPTION	PREP	CHKD	APPD	DATE
R02	FOR APPROVAL	STM	SAK	SAK	13/07/26
R01	FOR APPROVAL	STM	SAK	SAK	16/06/26
R00	FOR APPROVAL	STM	SAK	SAK	20/03/25
PROJECT					
KING KHALID INTERNATIONAL AIRPORT (KKIA) PROJECT CONCOURSE-A					
CLIENT					
ENGINEER					
CONTRACTOR					
DRAWING TITLE					
CCA-SS1-EMDB-1A					
DEVICE TAG LIST					
MANUFACTURER		DRAWING NO. CCA-SS1-EMDB-1A			
		PROJECT REFERENCE:			REC. 00
		SCALE : NTS		LOCATION: +2.1	SIZE: A4
		SHEET NO: 9 of 24			
QUOTATION REF.					
FILE NAME: 07_CCA-SS1-EMDB-1A					

Bill of Material

Order number	Qty.	Description	Make
3VA2463-5JP32-0AA0	1	circuit breaker 3VA2 IEC frame 630 breaking capacity class M Icu=55kA 415V 3-pole, line protection ETU550, LSI, In=630A overload protection Ir=250A...630A short-circuit protection Isd=0.6..9x In, Ii=1.5..9x In N conductor protection optionally with external current transformer, up to 160% nut keeper kit	SIEMENS
3VA9988-0AA12	1	AUXILIARY SWITCH CHANGEOVER CONTACTS TYPE HQ (7MM) ACCESSORY FOR 3VA-BREAKER 240VAC/250VDC 6A	SIEMENS
3VA9988-0AB12	1	TRIP ALARM SWITCH CHANGEOVER CONTACTS TYPE HQ (7MM) ACCESSORY FOR 3VA1 & 3VA20 UPTO 3VA25	SIEMENS
3VA9323-0KP00	1	Plug-in unit Complete kit Accessory for: Circuit breaker, 3-pole 3VA2 400/630	SIEMENS

REVISION					
REV	DESCRIPTION	PREP	CHKD	APPD	DATE

R02	FOR APPROVAL	STM	SAK	SAK	13/07/26
R01	FOR APPROVAL	STM	SAK	SAK	16/06/26
R00	FOR APPROVAL	STM	SAK	SAK	20/03/25

PROJECT	KING KHALID INTERNATIONAL AIRPORT (KKIA) PROJECT CONCOURSE-A
---------	--

CLIENT

ENGINEER

CONTRACTOR

DRAWING TITLE

CCA-SS1-EMDB-1A

SUNSHINE PARTS LIST

SUMMARIZED PARTS LIST			
MANUFACTURER	DRAWING NO. CCA-SS1-EMDB-1A		
	PROJECT REFERENCE:		REC. 00
	SCALE : NTS	LOCATION: +2.1	SIZE: A4
	SHEET NO: 10 of 24		

QUOTATION REF.

FILE NAME: 07_CCA-SS1-EMDB-1A

Device tag list

[illegible]

REVISION					
REV	DESCRIPTION	PREP	CHKD	APPD	DATE
R02	FOR APPROVAL	STM	SAK	SAK	13/07/26
R01	FOR APPROVAL	STM	SAK	SAK	16/06/26
R00	FOR APPROVAL	STM	SAK	SAK	20/03/25
PROJECT KING KHALID INTERNATIONAL AIRPORT (KKIA) PROJECT CONCOURSE-A					
CLIENT					
ENGINEER					
CONTRACTOR					
DRAWING TITLE CCA-SS1-EMDB-1A DEVICE TAG LIST					
MANUFACTURER		DRAWING NO. CCA-SS1-EMDB-1A			
		PROJECT REFERENCE:			REC. 00
		SCALE : NTS		LOCATION: +2.2	SIZE: A4
		SHEET NO: 11 of 24			
QUOTATION REF.					
FILE NAME: 07_CCA-SS1-EMDB-1A					

Bill of Material

Order number	Qty.	Description	Make
3VA2463-5JP32-0AA0	1	circuit breaker 3VA2 IEC frame 630 breaking capacity class M Icu=55kA 415V 3-pole, line protection ETU550, LSI, In=630A overload protection Ir=250A...630A short-circuit protection Isd=0.6..9x In, Ii=1.5..9x In N conductor protection optionally with external current transformer, up to 160% nut keeper kit	SIEMENS
3VA9988-0AA12	1	AUXILIARY SWITCH CHANGEOVER CONTACTS TYPE HQ (7MM) ACCESSORY FOR 3VA-BREAKER 240VAC/250VDC 6A	SIEMENS
3VA9988-0AB12	1	TRIP ALARM SWITCH CHANGEOVER CONTACTS TYPE HQ (7MM) ACCESSORY FOR 3VA1 & 3VA20 UPTO 3VA25	SIEMENS
3VA9323-0KP00	1	Plug-in unit Complete kit Accessory for: Circuit breaker, 3-pole 3VA2 400/630	SIEMENS

REVISION					
REV	DESCRIPTION	PREP	CHKD	APPD	DATE
R02	FOR APPROVAL	STM	SAK	SAK	13/07/26
R01	FOR APPROVAL	STM	SAK	SAK	16/06/26
R00	FOR APPROVAL	STM	SAK	SAK	20/03/25

PROJECT	KING KHALID INTERNATIONAL AIRPORT (KKIA) PROJECT CONCOURSE-A
---------	--

CLIENT _____

ENGINEER

CONTRACTOR

DRAWING TITLE

CCA-SS1-EMDB-1A

SUMMARY OF REVISIONS

SUMMARIZED PARTS LIST			
MANUFACTURER	DRAWING NO. CCA-SS1-EMDB-1A		
	PROJECT REFERENCE:		REC. 00
	SCALE : NTS	LOCATION: +2.2	SIZE: A4
	SHEET NO: 12 of 24		

QUOTATION REF.

FILE NAME: 07_CCA-SS1-EMDB-1A

Device tag list

[illegible]

REVISION					
REV	DESCRIPTION	PREP	CHKD	APPD	DATE
R02	FOR APPROVAL	STM	SAK	SAK	13/07/26
R01	FOR APPROVAL	STM	SAK	SAK	16/06/26
R00	FOR APPROVAL	STM	SAK	SAK	20/03/25
PROJECT KING KHALID INTERNATIONAL AIRPORT (KKIA) PROJECT CONCOURSE-A					
CLIENT					
ENGINEER					
CONTRACTOR					
DRAWING TITLE CCA-SS1-EMDB-1A DEVICE TAG LIST					
MANUFACTURER		DRAWING NO. CCA-SS1-EMDB-1A			
		PROJECT REFERENCE:			REC. 00
		SCALE : NTS		LOCATION: +2.3	SIZE: A4
		SHEET NO: 13 of 24			
QUOTATION REF.					
FILE NAME: 07_CCA-SS1-EMDB-1A					

Bill of Material

Order number	Qty.	Description	Make
3VA2340-5JP32-0AA0	1	CIRCUIT BREAKER 3VA2 IEC FRAME 400 BREAKING CAPACITY CLASS M ICU=55KA 415V 3-POLE, LINE PROTECTION ETU550, LSI, IN=400A OVERLOAD PROTECTION IR=160A...400A SHORT-CIRCUIT PROTECTION ISD=0.6..10X IN, II=1.5..10X IN N CONDUCTOR PROTECTION OPTIONALLY WITH EXTERNAL CURRENT TRANSFORMER, UP TO 160% NUT KEEPER KIT	SIEMENS
3VA9988-0AA12	1	AUXILIARY SWITCH CHANGEOVER CONTACTS TYPE HQ (7MM) ACCESSORY FOR 3VA-BREAKER 240VAC/250VDC 6A	SIEMENS
3VA9988-0AB12	1	TRIP ALARM SWITCH CHANGEOVER CONTACTS TYPE HQ (7MM) ACCESSORY FOR 3VA1 & 3VA20 UPTO 3VA25	SIEMENS
3VA9323-0KP00	1	Plug-in unit Complete kit Accessory for: Circuit breaker, 3-pole 3VA2 400/630	SIEMENS

REVISION					
REV	DESCRIPTION	PREP	CHKD	APPD	DATE
R02	FOR APPROVAL	STM	SAK	SAK	13/07/26
R01	FOR APPROVAL	STM	SAK	SAK	16/06/26
R00	FOR APPROVAL	STM	SAK	SAK	20/03/25

PROJECT	KING KHALID INTERNATIONAL AIRPORT (KKIA) PROJECT CONCOURSE-A
---------	--

CLIENT

ENGINEER

CONTRACTOR	

DRAWING TITLE

CCA-SS1-EMDB-1A

XXXXXXXXXXXXXXXXXXXX

SUMMARIZED PARTS LIST			
MANUFACTURER	DRAWING NO. CCA-SS1-EMDB-1A		
	PROJECT REFERENCE:		REC. 00
	SCALE : NTS	LOCATION: +2.3	SIZE: A4
	SHEET NO: 14 of 24		

QUOTATION REF.

FILE NAME: 07_CCA-SS1-EMDB-1A

Device tag list

	-Q4	+7.2°C
3VA2340-5JP32-0AA0		1
3VA9988-0AA12		1
3VA9988-0AB12		1
3VA9323-0KP00		1

REVISION					
REV	DESCRIPTION	PREP	CHKD	APPD	DATE
R02	FOR APPROVAL	STM	SAK	SAK	13/07/26
R01	FOR APPROVAL	STM	SAK	SAK	16/06/26
R00	FOR APPROVAL	STM	SAK	SAK	20/03/25
PROJECT					
KING KHALID INTERNATIONAL AIRPORT (KKIA) PROJECT CONCOURSE-A					
CLIENT					
ENGINEER					
CONTRACTOR					
DRAWING TITLE					
CCA-SS1-EMDB-1A					
DEVICE TAG LIST					
MANUFACTURER		DRAWING NO. CCA-SS1-EMDB-1A			
		PROJECT REFERENCE:			REC. 00
		SCALE : NTS		LOCATION: +2.4	SIZE: A4
		SHEET NO: 15 of 24			
QUOTATION REF.					
FILE NAME: 07_CCA-SS1-EMDB-1A					

Bill of Material

Order number	Qty.	Description	Make
3VA2340-5JP32-0AA0	1	CIRCUIT BREAKER 3VA2 IEC FRAME 400 BREAKING CAPACITY CLASS M ICU=55KA 415V 3-POLE, LINE PROTECTION ETU550, LSI, IN=400A OVERLOAD PROTECTION IR=160A...400A SHORT-CIRCUIT PROTECTION ISD=0.6..10X IN, II=1.5..10X IN N CONDUCTOR PROTECTION OPTIONALLY WITH EXTERNAL CURRENT TRANSFORMER, UP TO 160% NUT KEEPER KIT	SIEMENS
3VA9988-0AA12	1	AUXILIARY SWITCH CHANGEOVER CONTACTS TYPE HQ (7MM) ACCESSORY FOR 3VA-BREAKER 240VAC/250VDC 6A	SIEMENS
3VA9988-0AB12	1	TRIP ALARM SWITCH CHANGEOVER CONTACTS TYPE HQ (7MM) ACCESSORY FOR 3VA1 & 3VA20 UPTO 3VA25	SIEMENS
3VA9323-0KP00	1	Plug-in unit Complete kit Accessory for: Circuit breaker, 3-pole 3VA2 400/630	SIEMENS

REVISION					
REV	DESCRIPTION	PREP	CHKD	APPD	DATE
R02	FOR APPROVAL	STM	SAK	SAK	13/07/26
R01	FOR APPROVAL	STM	SAK	SAK	16/06/26
R00	FOR APPROVAL	STM	SAK	SAK	20/03/25

PROJECT	KING KHALID INTERNATIONAL AIRPORT (KKIA) PROJECT CONCOURSE-A
---------	--

CLIENT

ENGINEER

CONTRACTOR	

DRAWING TITLE

CCA-SS1-EMDB-1A

XXXXXXXXXXXXXXXXXXXX

SUMMARIZED PARTS LIST			
MANUFACTURER	DRAWING NO. CCA-SS1-EMDB-1A		
	PROJECT REFERENCE:		REC. 00
	SCALE : NTS	LOCATION: +2.4	SIZE: A4
	SHEET NO: 16 of 24		

QUOTATION REF.


FILE NAME: 07_CCA-SS1-EMDB-1A


Device tag list

-Q5	+7.4°C
3VA2340-5JP32-0AA0	1
3VA9988-0AA12	1
3VA9988-0AB12	1
3VA9323-0KP00	1

REVISION					
REV	DESCRIPTION	PREP	CHKD	APPD	DATE
R02	FOR APPROVAL	STM	SAK	SAK	13/07/26
R01	FOR APPROVAL	STM	SAK	SAK	16/06/26
R00	FOR APPROVAL	STM	SAK	SAK	20/03/25
PROJECT KING KHALID INTERNATIONAL AIRPORT (KKIA) PROJECT CONCOURSE-A					
CLIENT					
ENGINEER					
CONTRACTOR					
DRAWING TITLE CCA-SS1-EMDB-1A DEVICE TAG LIST					
MANUFACTURER		DRAWING NO. CCA-SS1-EMDB-1A			
		PROJECT REFERENCE:			REC. 00
		SCALE : NTS		LOCATION: +2.5	SIZE: A4
		SHEET NO: 17 of 24			
QUOTATION REF.					
FILE NAME: 07_CCA-SS1-EMDB-1A					

1	2	3	4	5	6	7	8	9	10
A	Bill of Material								
B									
C									
D									
E									
F									
G									
H									

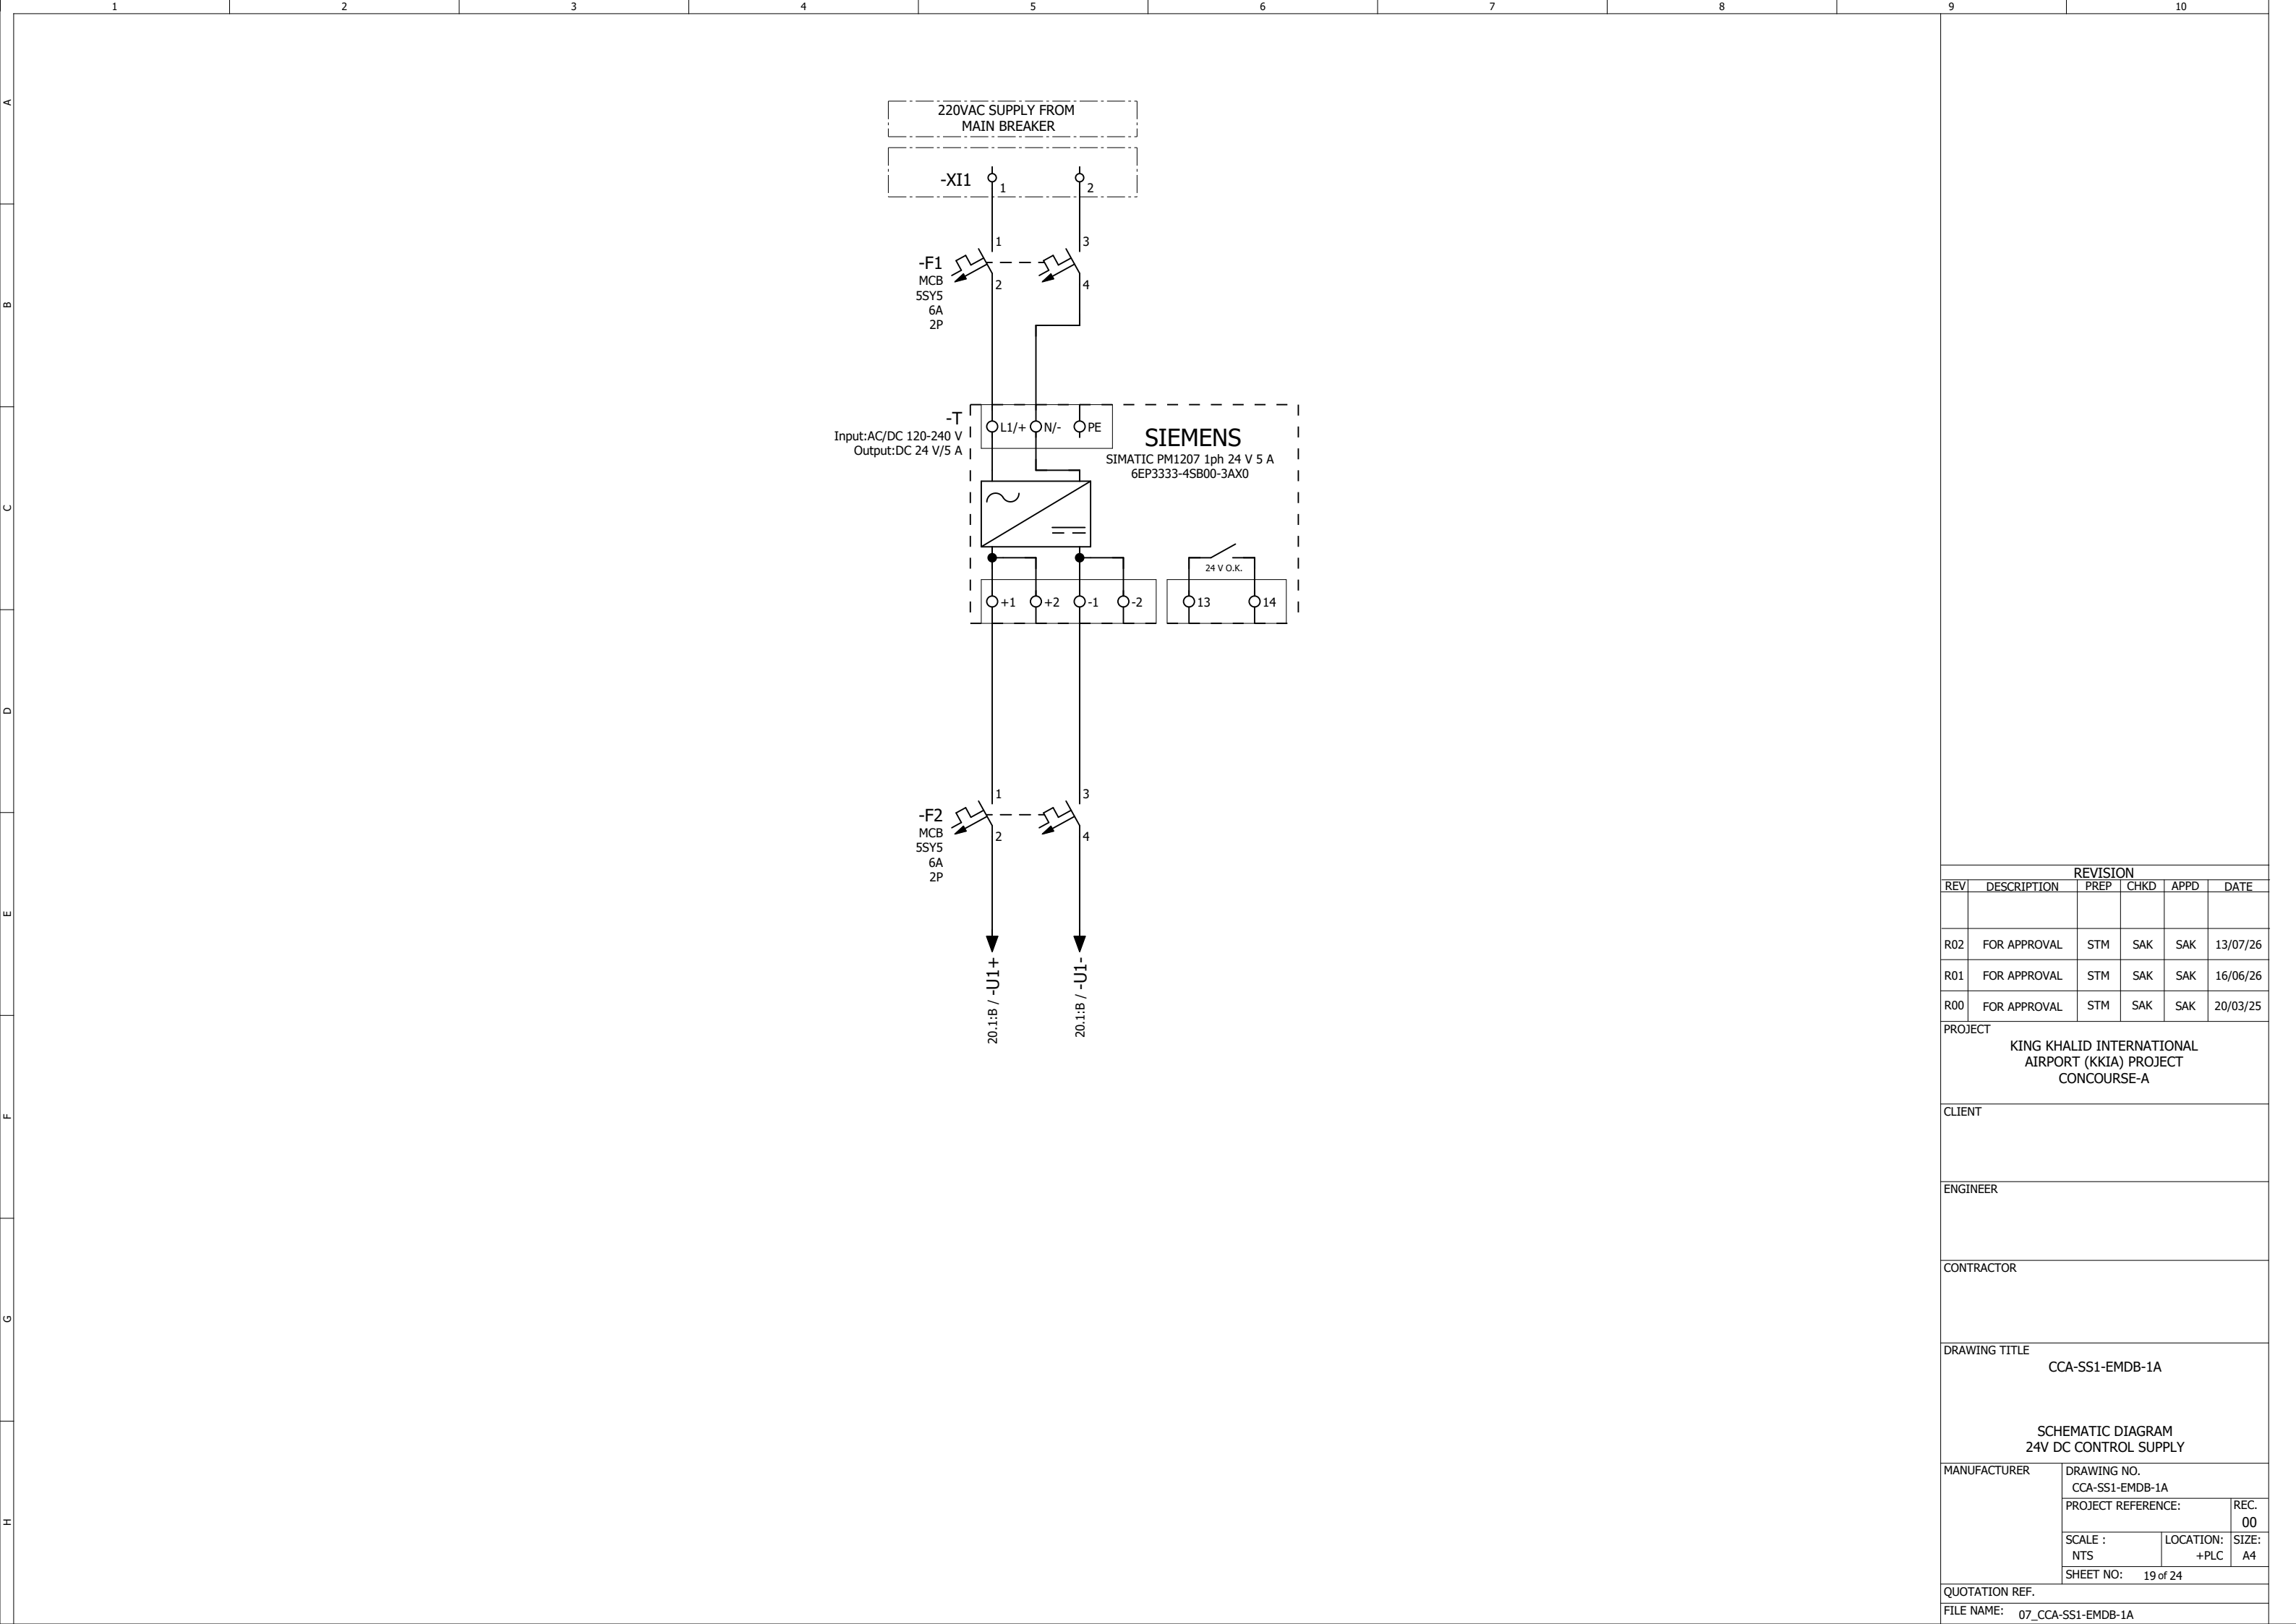

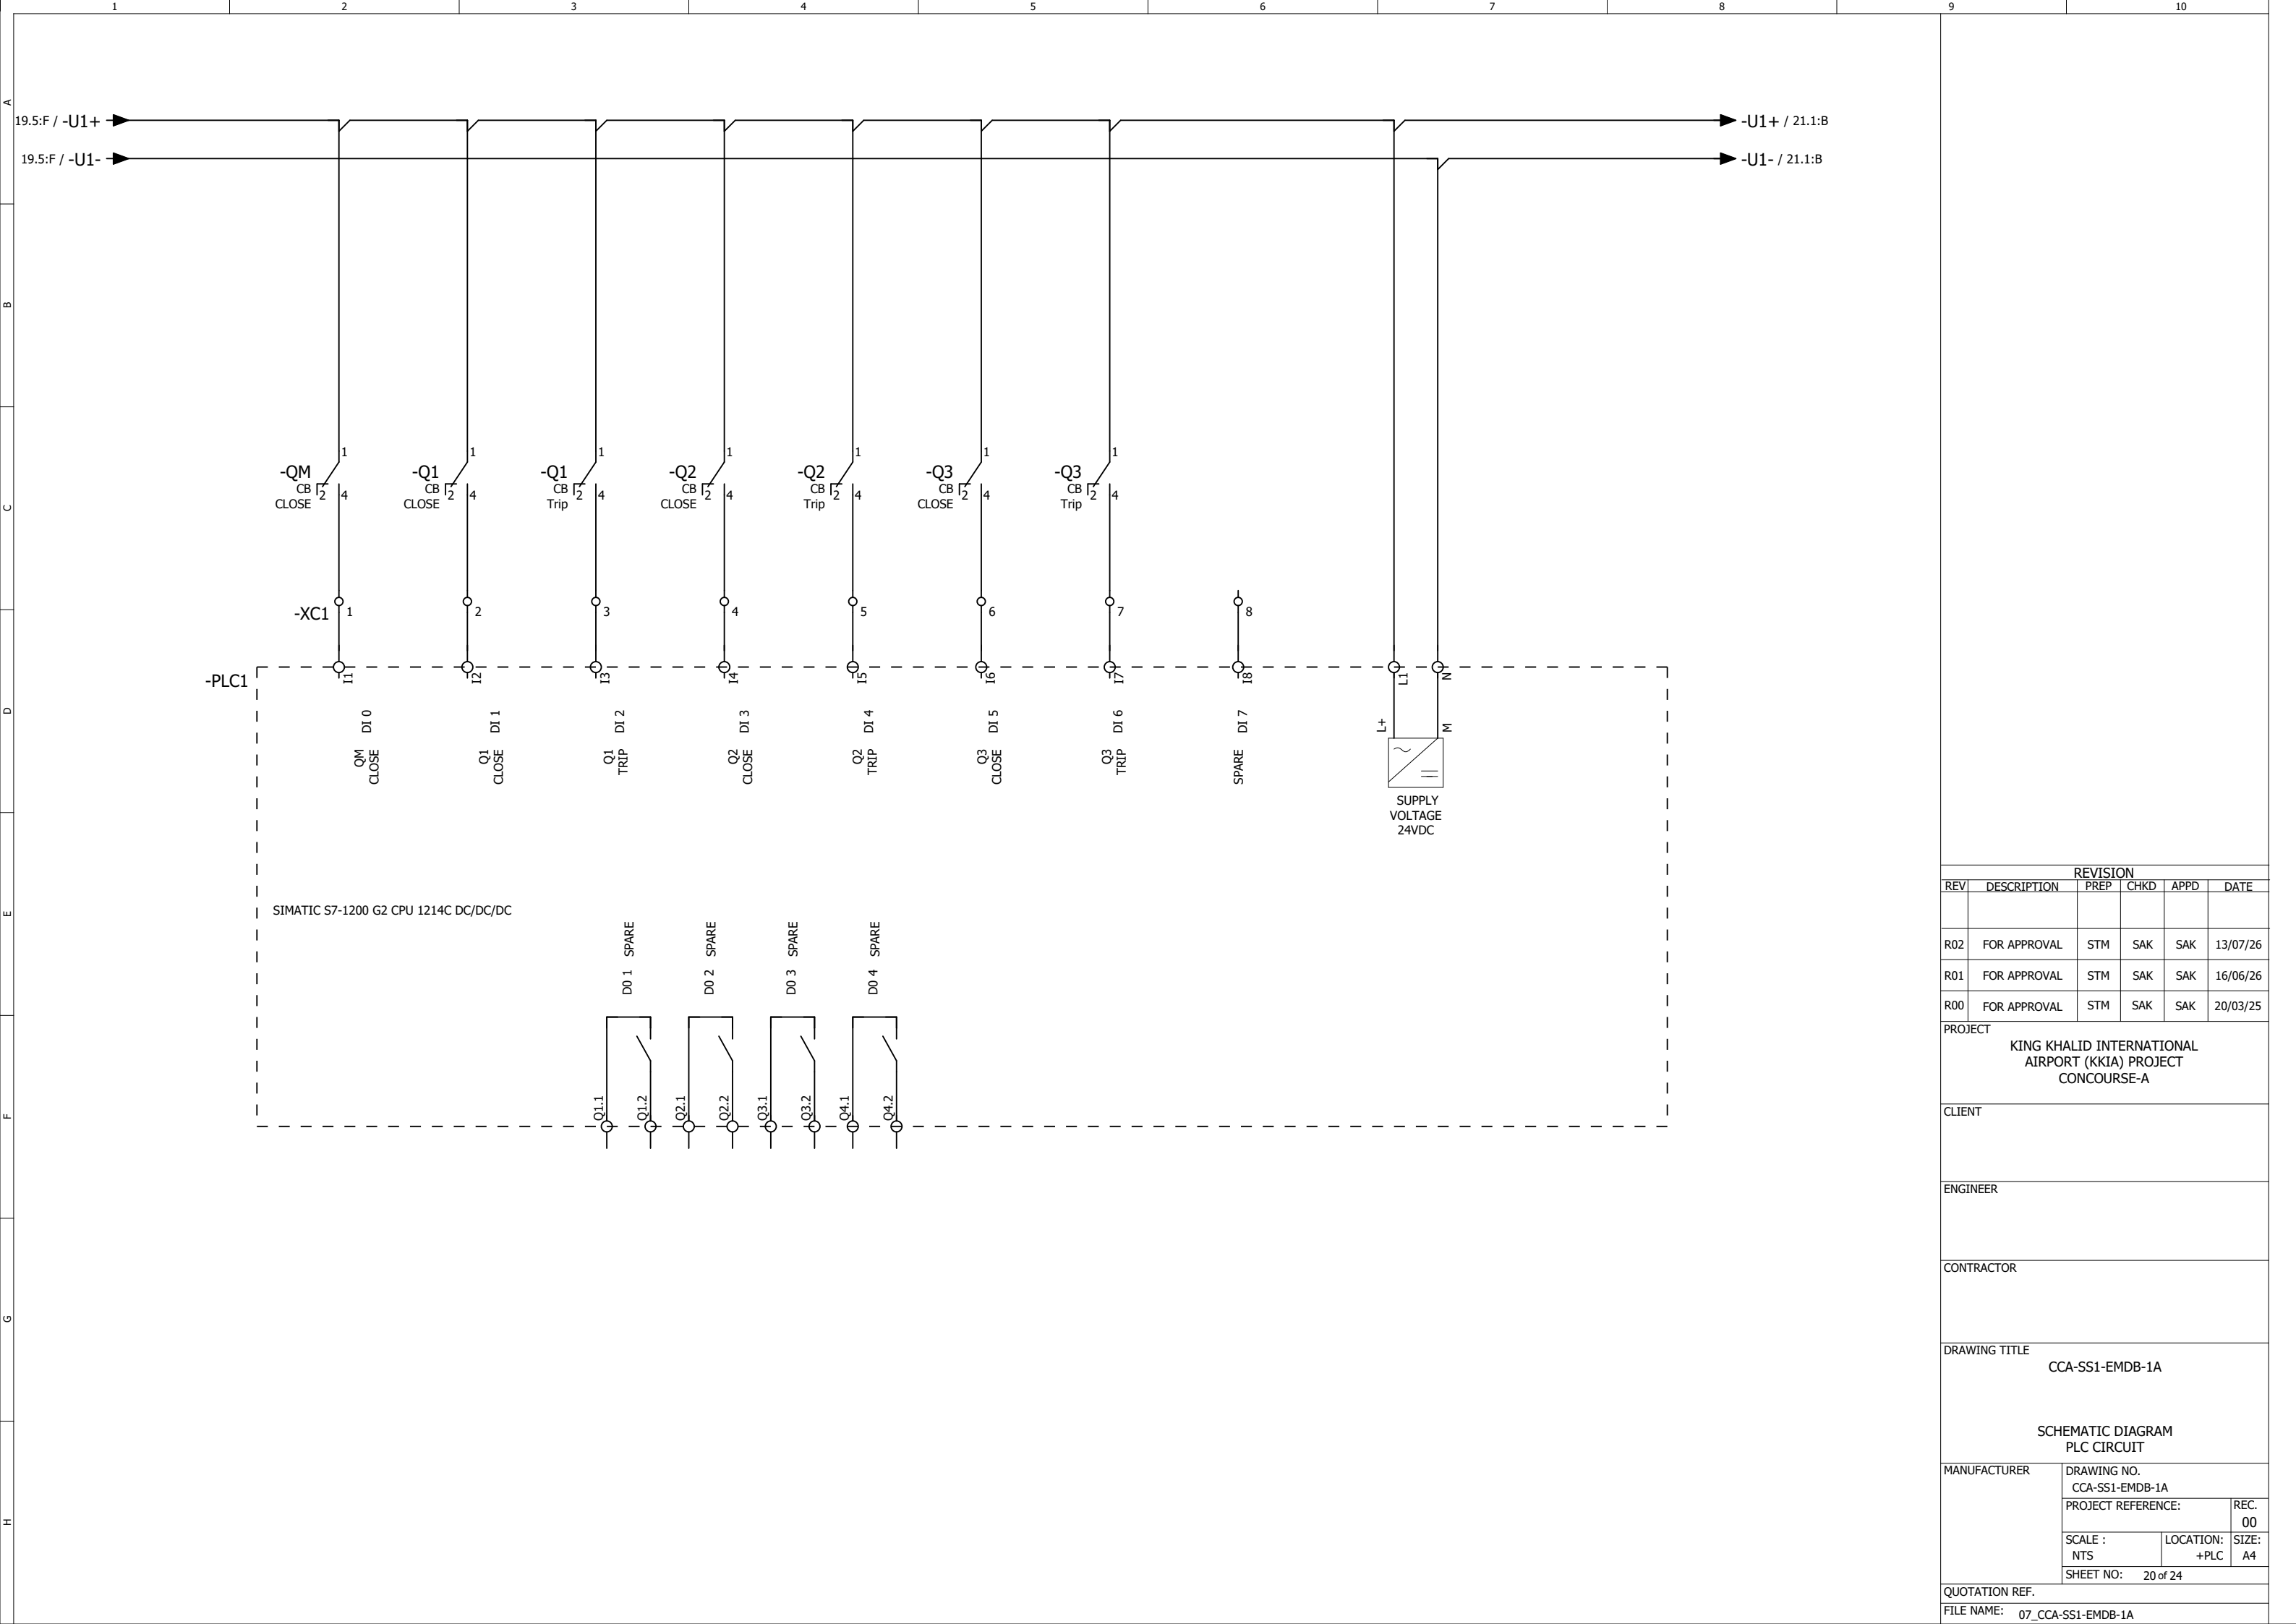

REVISION					
REV	DESCRIPTION	PREP	CHKD	APPD	DATE

R02	FOR APPROVAL	STM	SAK	SAK	13/07/26
R01	FOR APPROVAL	STM	SAK	SAK	16/06/26
R00	FOR APPROVAL	STM	SAK	SAK	20/03/25

PROJECT

KING KHALID INTERNATIONAL
AIRPORT (KKIA) PROJECT
CONCOURSE-A

CLIENT

ENGINEER

CONTRACTOR


DRAWING TITLE

CCA-SS1-EMDB-1A

MANUFACTURER	DRAWING NO. CCA-SS1-EMDB-1A		
	PROJECT REFERENCE:		REC. 00
	SCALE : NTS	LOCATION: +PLC	SIZE: A4
	SHEET NO: 20 of 24		

QUOTATION REF.



FILE NAME: 07_CCA-SS1-EMDB-1A

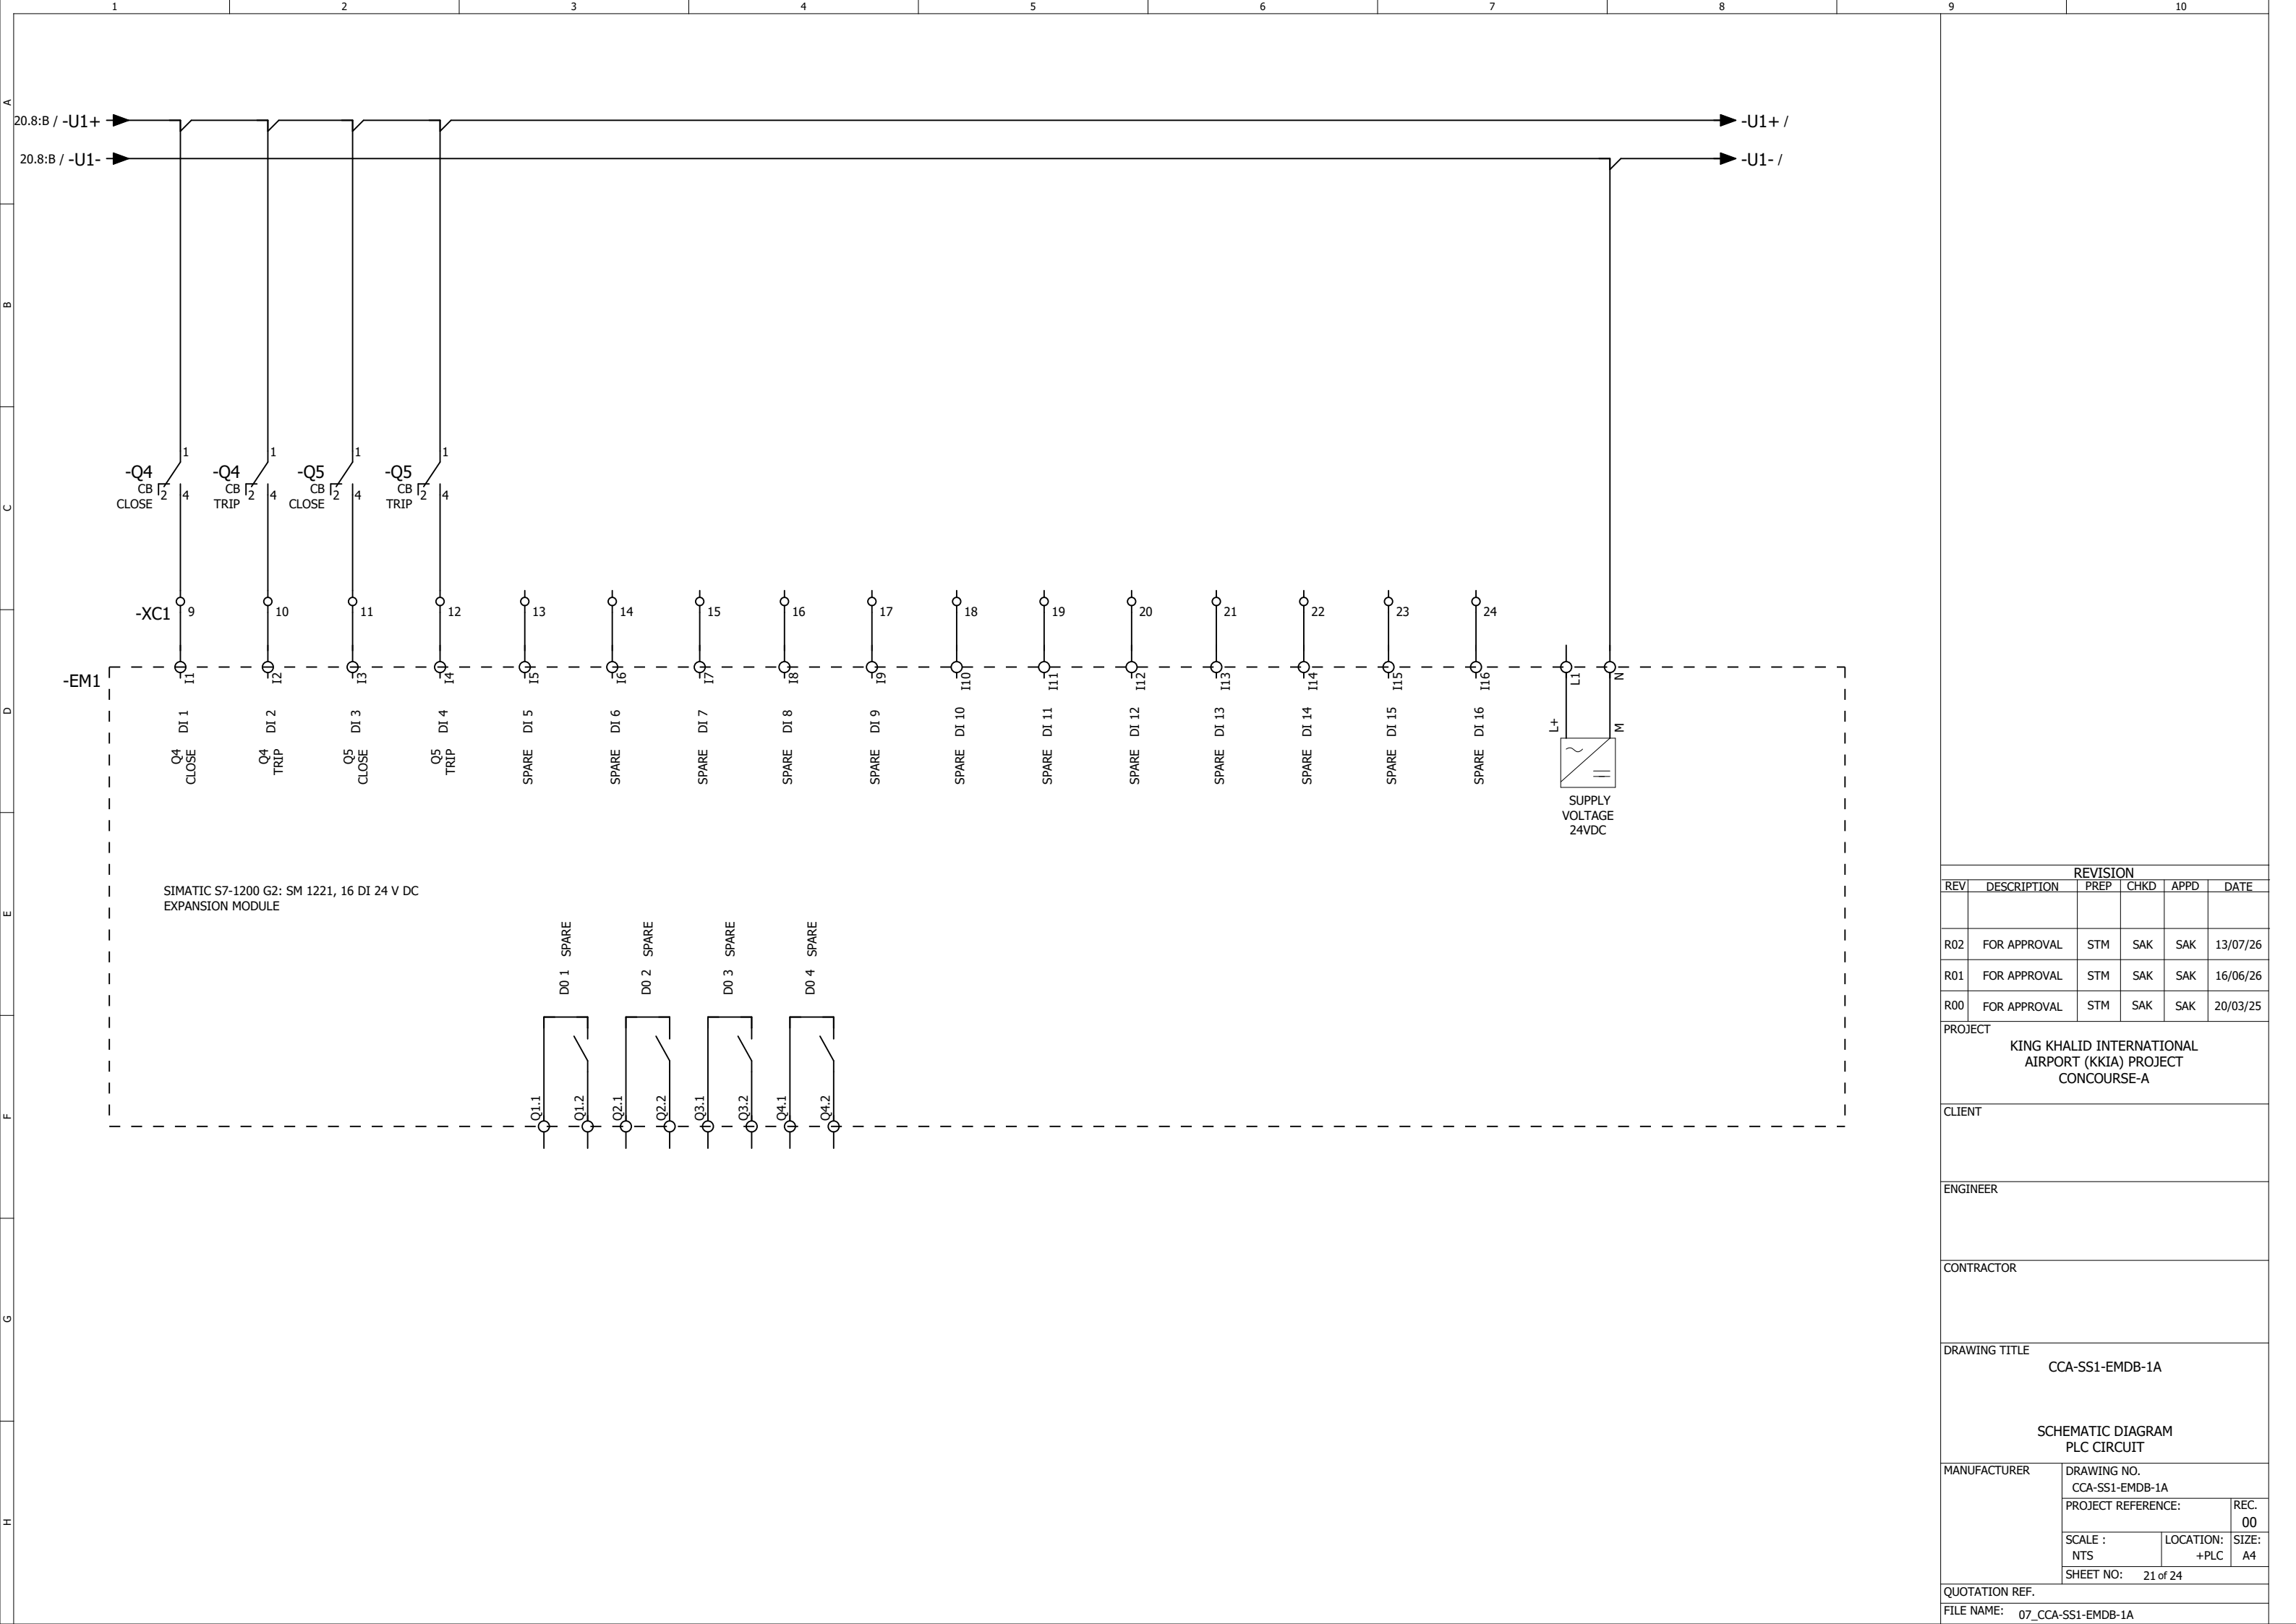

REVISION					
REV	DESCRIPTION	PREP	CHKD	APPD	DATE
R02	FOR APPROVAL	STM	SAK	SAK	13/07/26
R01	FOR APPROVAL	STM	SAK	SAK	16/06/26
R00	FOR APPROVAL	STM	SAK	SAK	20/03/25
PROJECT KING KHALID INTERNATIONAL AIRPORT (KKIA) PROJECT CONCOURSE-A					
CLIENT					
ENGINEER					
CONTRACTOR					
DRAWING TITLE CCA-SS1-EMDB-1A SCHEMATIC DIAGRAM PLC CIRCUIT					
MANUFACTURER		DRAWING NO. CCA-SS1-EMDB-1A			REC. 00
		PROJECT REFERENCE:			
		SCALE : NTS		LOCATION: +PLC	
		SHEET NO: 21 of 24			
QUOTATION REF.					
FILE NAME: 07_CCA-SS1-EMDB-1A					

Terminal diagram

Strip: =07_CCA-SS1-EMDB-1A+-XC1

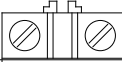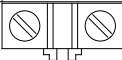External targets						Internal targets				
Target designation	Wiring	Jumper		SD		Jumper	Wiring	Target designation	Placement	Function text
				1				-QM:4	/9.2:C	IC1 INPUTS TO PLC
				2				-Q1:4	/9.2:C	=
				3				-Q1:4	/9.3:C	=
				4				-Q2:4	/9.4:C	=
				5				-Q2:4	/9.4:C	=
				6				-Q3:4	/9.5:C	=
				7				-Q3:4	/9.5:C	=
				8						=
				9				-Q4:4	/10.1:C	=
				10				-Q4:4	/10.2:C	=
				11				-Q5:4	/10.2:C	=
				12				-Q5:4	/10.2:C	=
				13						=
				14						=
				15						=
				16						=
				17						=
				18						=
				19						=
				20						=
				21						=
				22						=
				23						=
				24						=
										

Strip: =07_CCA-SS1-EMDB-1A+-XI1

External targets			Internal targets						
Target designation	Wiring	Jumper		SD	Jumper	Wiring	Target designation	Placement	Function text
				1			-F1:1	/8.5:B	EXTERNAL 110VDC SUPPLY FROM DC CHARGER
				2			-F1:3	/8.5:B	=
									

REVISION					
REV	DESCRIPTION	PREP	CHKD	APPD	DATE
R02	FOR APPROVAL	STM	SAK	SAK	13/07/26
R01	FOR APPROVAL	STM	SAK	SAK	16/06/26
R00	FOR APPROVAL	STM	SAK	SAK	20/03/25

PROJECT KING KHALID INTERNATIONAL AIRPORT (KKIA) PROJECT CONCOURSE-A			
CLIENT			
ENGINEER			
CONTRACTOR			
DRAWING TITLE CCA-SS1-EMDB-1A TERMINAL LINE-UP DIAGRAM			
MANUFACTURER	DRAWING NO. CCA-SS1-EMDB-1A		
	PROJECT REFERENCE:		REC. 00
	SCALE : NTS	LOCATION: +PLC	SIZE: A4
	SHEET NO: 22 of 24		
QUOTATION REF.			
FILE NAME: 07_CCA-SS1-EMDB-1A			

1	2	3	4	5	6	7	8	9	10	
A	Device tag list	
B	
C	
D	
E	
F	
G	
H	
<table><tr><td colspan="2">6ES7221-1BH50-0XB0</td><td colspan="2">-EM1</td><td colspan="2">/10.1:D</td></tr><tr><td colspan="2"></td><td colspan="2"></td><td colspan="2">1</td></tr></table>										6ES7221-1BH50-0XB0		-EM1		/10.1:D						1	
6ES7221-1BH50-0XB0		-EM1		/10.1:D	
				1	
<table><tr><td colspan="2">5SY5206-7</td><td colspan="2">-F1</td><td colspan="2">/8.5:B</td></tr><tr><td colspan="2"></td><td colspan="2"></td><td colspan="2">1</td></tr></table>										5SY5206-7		-F1		/8.5:B						1	
5SY5206-7		-F1		/8.5:B	
				1	
<table><tr><td colspan="2">5SY5206-7</td><td colspan="2">-F2</td><td colspan="2">/8.5:E</td></tr><tr><td colspan="2"></td><td colspan="2"></td><td colspan="2">1</td></tr></table>										5SY5206-7		-F2		/8.5:E						1	
5SY5206-7		-F2		/8.5:E	
				1	
<table><tr><td colspan="2">6ES7214-1AH50-0XB0</td><td colspan="2">-PLC1</td><td colspan="2">/9.2:D</td></tr><tr><td colspan="2"></td><td colspan="2"></td><td colspan="2">1</td></tr></table>										6ES7214-1AH50-0XB0		-PLC1		/9.2:D						1	
6ES7214-1AH50-0XB0		-PLC1		/9.2:D	
				1	
<table><tr><td colspan="2">6EP3333-4SB00-3AX0</td><td colspan="2">-T</td><td colspan="2">/8.5:C</td></tr><tr><td colspan="2"></td><td colspan="2"></td><td colspan="2">1</td></tr></table>										6EP3333-4SB00-3AX0		-T		/8.5:C						1	
6EP3333-4SB00-3AX0		-T		/8.5:C	
				1	
<table><tr><th colspan="6">REVISION</th></tr><tr><th>REV</th><th>DESCRIPTION</th><th>PREP</th><th>CHKD</th><th>APPD</th><th>DATE</th></tr><tr><td></td><td></td><td></td><td></td><td></td><td></td></tr><tr><td>R02</td><td>FOR APPROVAL</td><td>STM</td><td>SAK</td><td>SAK</td><td>13/07/26</td></tr><tr><td>R01</td><td>FOR APPROVAL</td><td>STM</td><td>SAK</td><td>SAK</td><td>16/06/26</td></tr><tr><td>R00</td><td>FOR APPROVAL</td><td>STM</td><td>SAK</td><td>SAK</td><td>20/03/25</td></tr><tr><td colspan="6">PROJECT KING KHALID INTERNATIONAL AIRPORT (KKIA) PROJECT CONCOURSE-A</td></tr><tr><td colspan="6">CLIENT</td></tr><tr><td colspan="6">ENGINEER</td></tr><tr><td colspan="6">CONTRACTOR</td></tr><tr><td colspan="6">DRAWING TITLE CCA-SS1-EMDB-1A DEVICE TAG LIST</td></tr><tr><td colspan="2" rowspan="4">MANUFACTURER</td><td colspan="4">DRAWING NO. CCA-SS1-EMDB-1A</td></tr><tr><td colspan="3">PROJECT REFERENCE:</td><td>REC. 00</td></tr><tr><td>SCALE : NTS</td><td>LOCATION: +PLC</td><td>SIZE: A4</td></tr><tr><td colspan="3">SHEET NO: 23 of 24</td></tr><tr><td colspan="6">QUOTATION REF.</td></tr><tr><td colspan="6">FILE NAME: 07_CCA-SS1-EMDB-1A</td></tr></table>										REVISION						REV	DESCRIPTION	PREP	CHKD	APPD	DATE							R02	FOR APPROVAL	STM	SAK	SAK	13/07/26	R01	FOR APPROVAL	STM	SAK	SAK	16/06/26	R00	FOR APPROVAL	STM	SAK	SAK	20/03/25	PROJECT KING KHALID INTERNATIONAL AIRPORT (KKIA) PROJECT CONCOURSE-A						CLIENT						ENGINEER						CONTRACTOR						DRAWING TITLE CCA-SS1-EMDB-1A DEVICE TAG LIST						MANUFACTURER		DRAWING NO. CCA-SS1-EMDB-1A				PROJECT REFERENCE:			REC. 00	SCALE : NTS	LOCATION: +PLC	SIZE: A4	SHEET NO: 23 of 24			QUOTATION REF.						FILE NAME: 07_CCA-SS1-EMDB-1A					
REVISION	
REV	DESCRIPTION	PREP	CHKD	APPD	DATE	
R02	FOR APPROVAL	STM	SAK	SAK	13/07/26	
R01	FOR APPROVAL	STM	SAK	SAK	16/06/26	
R00	FOR APPROVAL	STM	SAK	SAK	20/03/25	
PROJECT KING KHALID INTERNATIONAL AIRPORT (KKIA) PROJECT CONCOURSE-A	
CLIENT	
ENGINEER	
CONTRACTOR	
DRAWING TITLE CCA-SS1-EMDB-1A DEVICE TAG LIST	
MANUFACTURER		DRAWING NO. CCA-SS1-EMDB-1A	
		PROJECT REFERENCE:			REC. 00	
		SCALE : NTS	LOCATION: +PLC	SIZE: A4	
		SHEET NO: 23 of 24	
QUOTATION REF.	
FILE NAME: 07_CCA-SS1-EMDB-1A	

6ES7221-1BH50-0XB0	-EM1	/10.1:D	1
5SY5206-7	-F1	/8.5:B	1
5SY5206-7	-F2	/8.5:E	1
6ES7214-1AH50-0XB0	-PLC1	/9.2:D	1
6EP3333-4SB00-3AX0	-T	/8.5:C	1

Bill of Material

Order number	Qty.	Description	Make
6ES7221-1BH50-0XB0	1	SIMATIC S7-1200 G2: SM 1221 digital input, 16 DI; inputs: 16x DI 24 V DC sink/source	SIEMENS
5SY5206-7	2	Circuit breaker Universal current 440 V DC 400 V AC 10kA, 2-pole, C, 6A	SIEMENS
6ES7214-1AH50-0XB0	1	SIMATIC S7-1200 G2: compact CPU 1214C DC/DC/DC; power supply: DC 20.4-28.8 V DC; onboard I/O: 14x DI 24 V DC; 10 DO 24 V DC; memory: program 250 KB data: 750 KB, retentivity: 20 KB	SIEMENS
6EP3333-4SB00-3AX0	1	SIMATIC S7-1200 power module PM 1207 24 V/5 A stabilized power supply Input: AC/DC 120 - 240 V Output: DC 24 V/5 A with UDI diagnostic interface	SIEMENS
CTS2.5UN	26	2.5 SQ.MM, 5 MM THICK FEED THROUGH TERMINAL BLOCK	CONNECTWELL

REVISION					
REV	DESCRIPTION	PREP	CHKD	APPD	DATE

R02	FOR APPROVAL	STM	SAK	SAK	13/07/26
R01	FOR APPROVAL	STM	SAK	SAK	16/06/26
R00	FOR APPROVAL	STM	SAK	SAK	20/03/25

PROJECT	KING KHALID INTERNATIONAL AIRPORT (KKIA) PROJECT CONCOURSE-A
---------	--

CLIENT

ENGINEER

CONTRACTOR

DRAWING TITLE
CCA-SS1-EMDB-1A

SUMMARIZED PARTS LIST			
MANUFACTURER	DRAWING NO. CCA-SS1-EMDB-1A		
	PROJECT REFERENCE:		REC. 00
	SCALE : NTS	LOCATION: +PLC	SIZE: A4
	SHEET NO: 24 of 24		

QUOTATION REF.

FILE NAME: 07_CCA-SS1-EMDB-1A